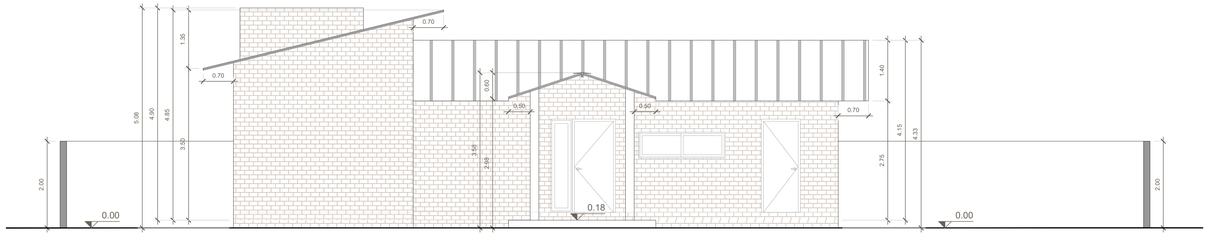

Fachada Norte
escala 1:50

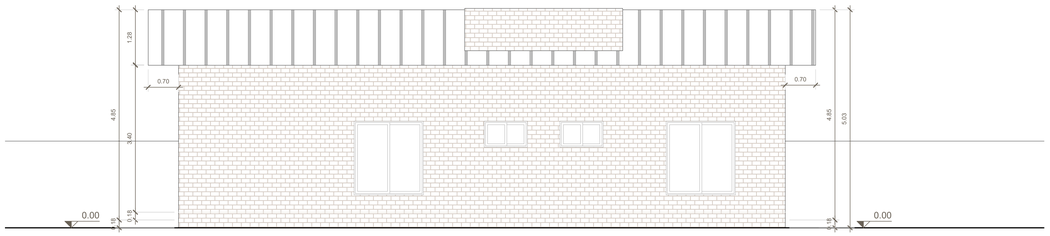

Fachada Leste
escala 1:50

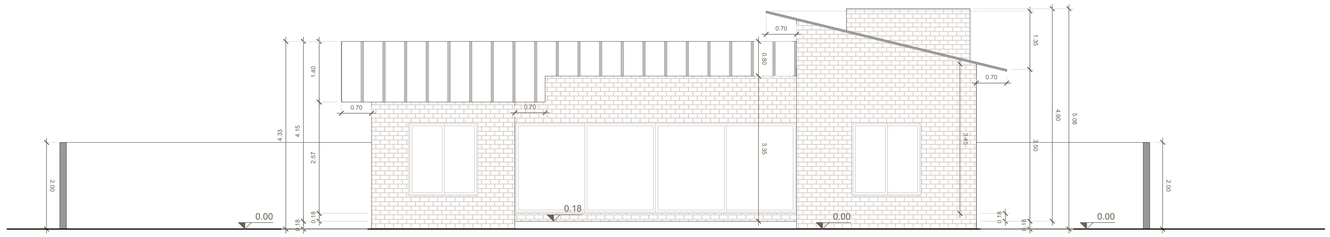

Fachada Sul
escala 1:50

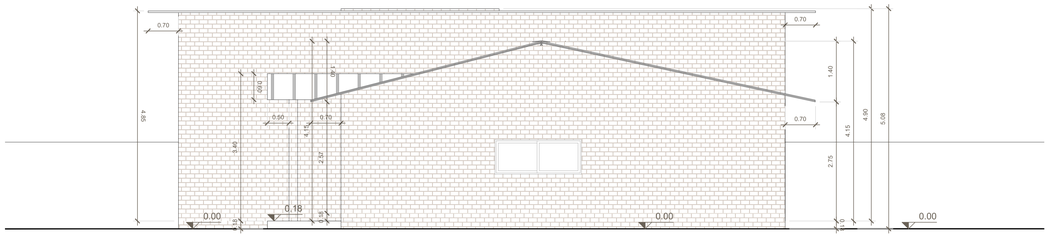

Fachada Oeste
escala 1:50

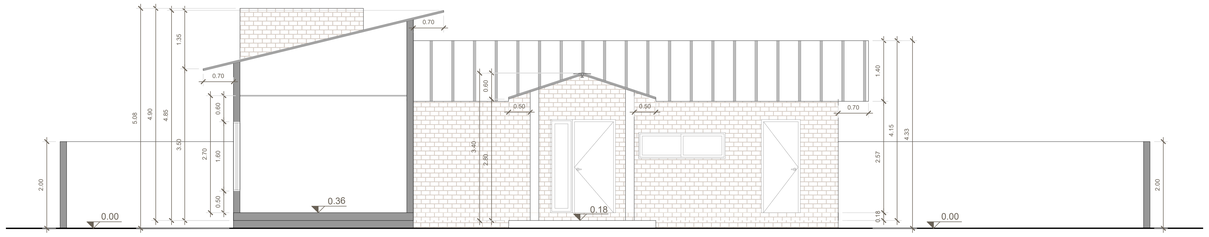

Corte BB
escala 1:50

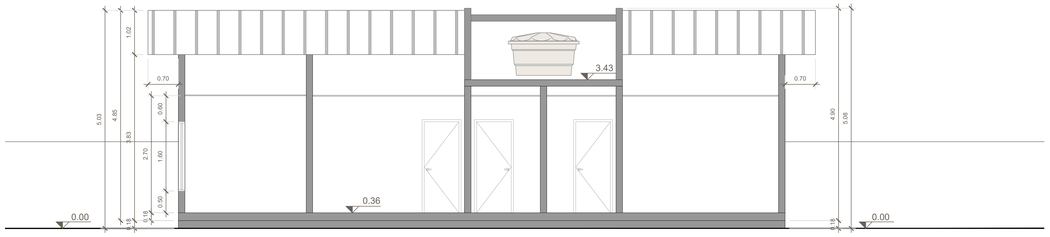

Corte AA
escala 1:50

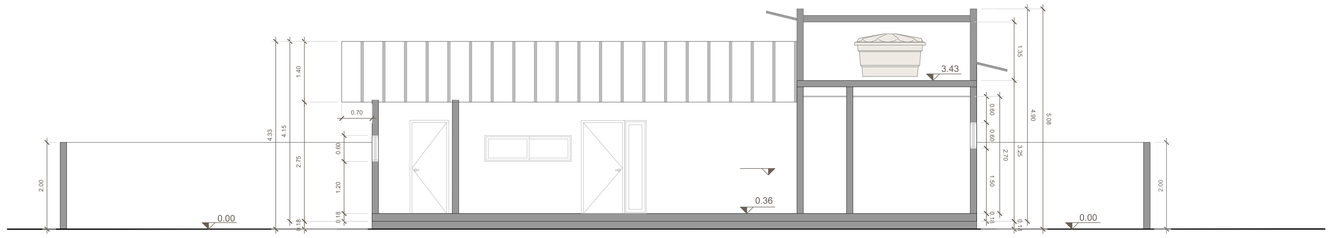

Corte CC
escala 1:50

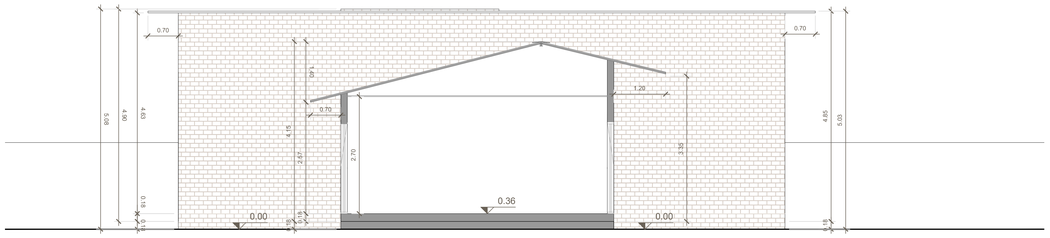

Corte DD
escala 1:50

KANTI
ARQUITETURA

tatianamoritanobre@gmail.com
Fone: (41) 99187-1888

Descrição:
CONSTRUÇÃO DE RESIDÊNCIA UNIFAMILIAR EM ALVENARIA

Escala: **1:50**

Data: **03 / 2026**

Referência: **ELEVAÇÕES**
CORTES

Desenho:
TATIANA MORITA NOBRE MATTOS
tatianamoritanobre@gmail.com
Fone: (41) 99187-1888

PROJETO ARQUITETÔNICO

Autor do projeto / Responsável técnico: TATIANA MORITA NOBRE MATTOS	CAU/PR: A42624-5	Assinatura:
Responsável pela execução:	CREA/PR:	Assinatura:
Proprietário(s): JORGYANO BRUNO DE OLIVEIRA VIEIRA	CPF: 061.044.724-60	Assinatura:
Proprietário(s):	CNPJ:	Assinatura:

Importante:
ESTE PROJETO NÃO PODERÁ SER REPRODUZIDO PARA OUTROS FINS SEM A EXPRESSA AUTORIZAÇÃO DO RESPONSÁVEL TÉCNICO ACIMA DESCRITO

Prancha: 02/02

FOLHA A0